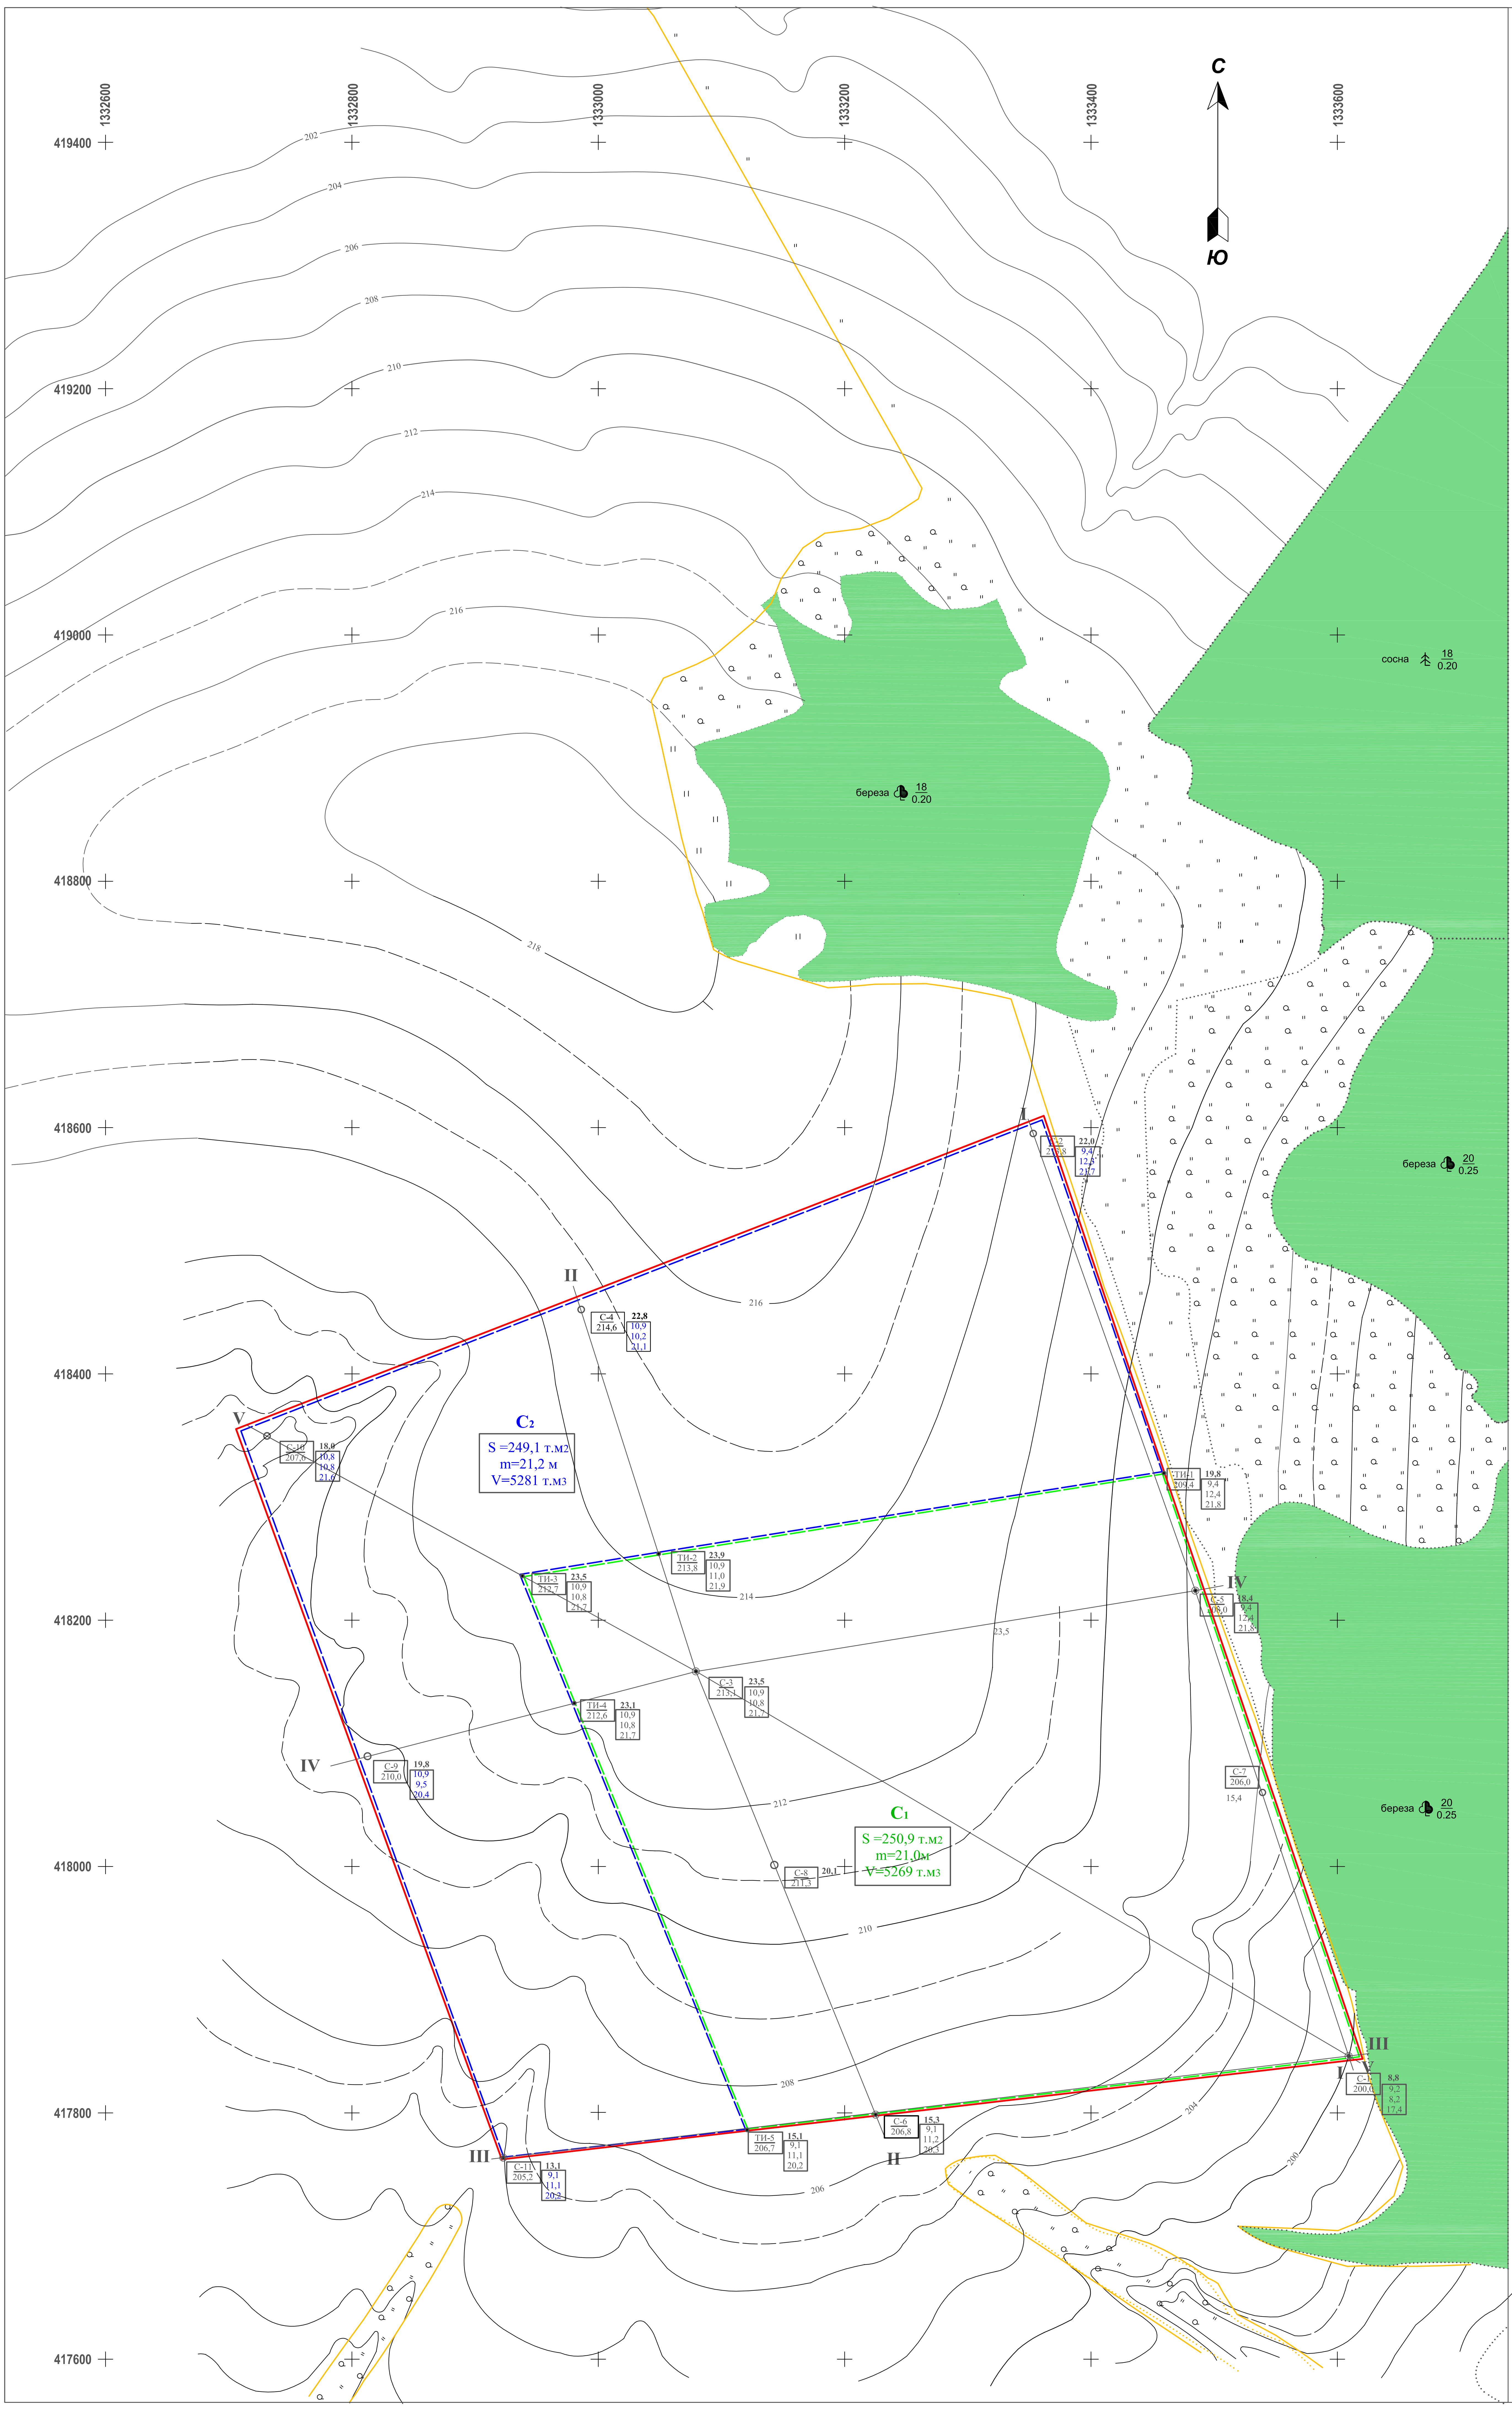
С
Ю
1332600
1332800
1333000
1333200
1333400
1333600
419400
419200
419000
418800
418600
418400
418200
418000
417800
417600
202
204
206
208
210
212
214
216
218
береза 18 0.20
сосна 18 0.20
береза 20 0.25
береза 20 0.25
I
II
III
IV
V
С-2 213,8 22,0 9,4 12,3 21,7
С-4 214,6 22,8 10,9 10,2 21,1
С-10 207,6 18,0 10,8 10,8 21,6
C2
S =249,1 т.м2
m=21,2 м
V=5281 т.м3
ТИ-1 209,4 19,8 9,4 12,4 21,8
ТИ-2 213,8 23,9 10,9 11,0 21,9
ТИ-3 212,7 23,5 10,9 10,8 21,7
С-5 208,0 18,4 9,4 12,4 21,8
23,5
С-3 213,1 23,5 10,9 10,8 21,7
ТИ-4 212,6 23,1 10,9 10,8 21,7
С-9 210,0 19,8 10,9 9,5 20,4
С-7 206,0 15,4
C1
S =250,9 т.м2
m=21,0м
V=5269 т.м3
С-8 211,3 20,1
С-1 200,0 8,8 9,2 8,2 17,4
С-6 206,8 15,3 9,1 11,2 20,3
ТИ-5 206,7 15,1 9,1 11,1 20,2
С-11 205,2 13,1 9,1 11,1 20,2

Условные обозначения

С-4 / 214,6	Номер скважины Абсолютная отметка устья,м
22,8 10,9 10,2 21,1	Мощность вскрышных пород, м Мощность известняков тарусско-венёвского горизонта (кат. C_2) Мощность известняков михайловского горизонта (кат. C_2), м Суммарная мощность известняков полезной толщи по кат. C_2
10,9 10,8 21,7	Мощность известняков тарусско-венёвского горизонта, м Мощность известняков михайловского горизонта, м Суммарная мощность известняков полезной толщи, м
⊙	Разведочные скважины 2009 г.
○	Вскрышные скважины, пробуренные в 2009 г.
•	Точка интерполяции
ТИ-3 / 212,7	Номер точки интерполяции и ее абсолютная отметка
I — I	Линии геологических разрезов и их номера
🟨	Граница земельного отвода ООО Сельскохозяйственное предприятие "Агротехпром"
🟥	Граница предварительного горного отвода
🟩	Контуры подсчёта запасов по категории С1
🟦	Контуры подсчёта запасов по категории С2
C_2	Категория запасов
S =249,1 т.м2	Площадь подсчетного блока
m=21,2 м	Мощность полезной толщи
V=5281 т.м3	Объем строительных известняков

					ООО Сельскохозяйственное предприятие "Агротехпром"		
					Разработка и рекультивация Марухтинского-2 месторождения строительных известняков		
Изм.	Лист	№ докум	Подпись	Дата			
					План поверхности и подсчета запасов строительных известняков	Стадия	Лист	Лислов
Маркшейдер		Телков Ю.В.				ТП	1	1
					Масштаб 1:2000	ООО НПП "Центр-недра"		