ГЕОЛОГИЧЕСКИЙ РАЗРЕЗ ПО ЛИНИИ 1-1

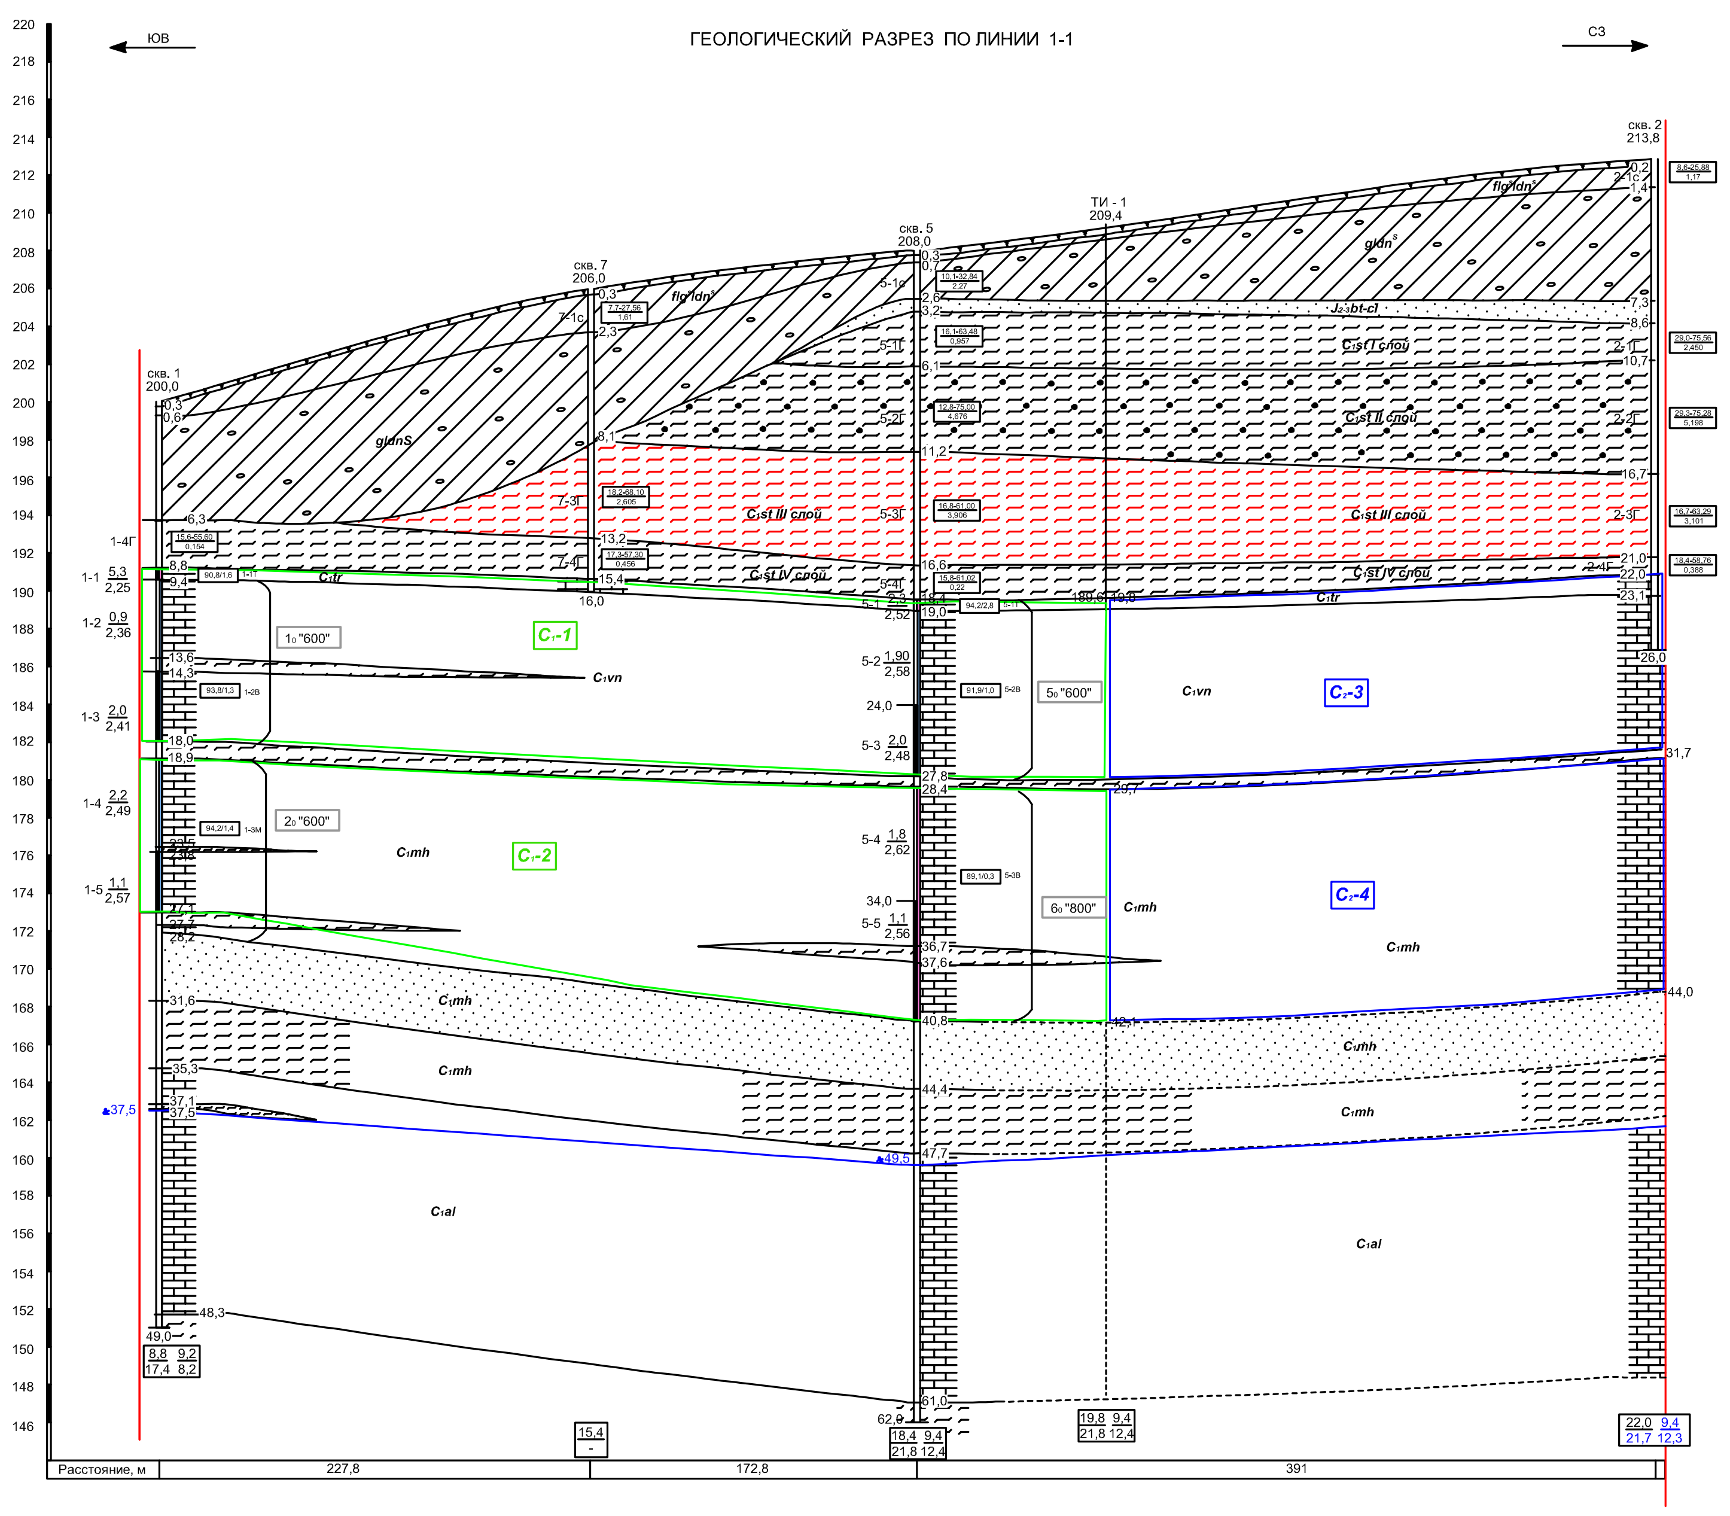

ГЕОЛОГИЧЕСКИЙ РАЗРЕЗ ПО ЛИНИИ 2-2

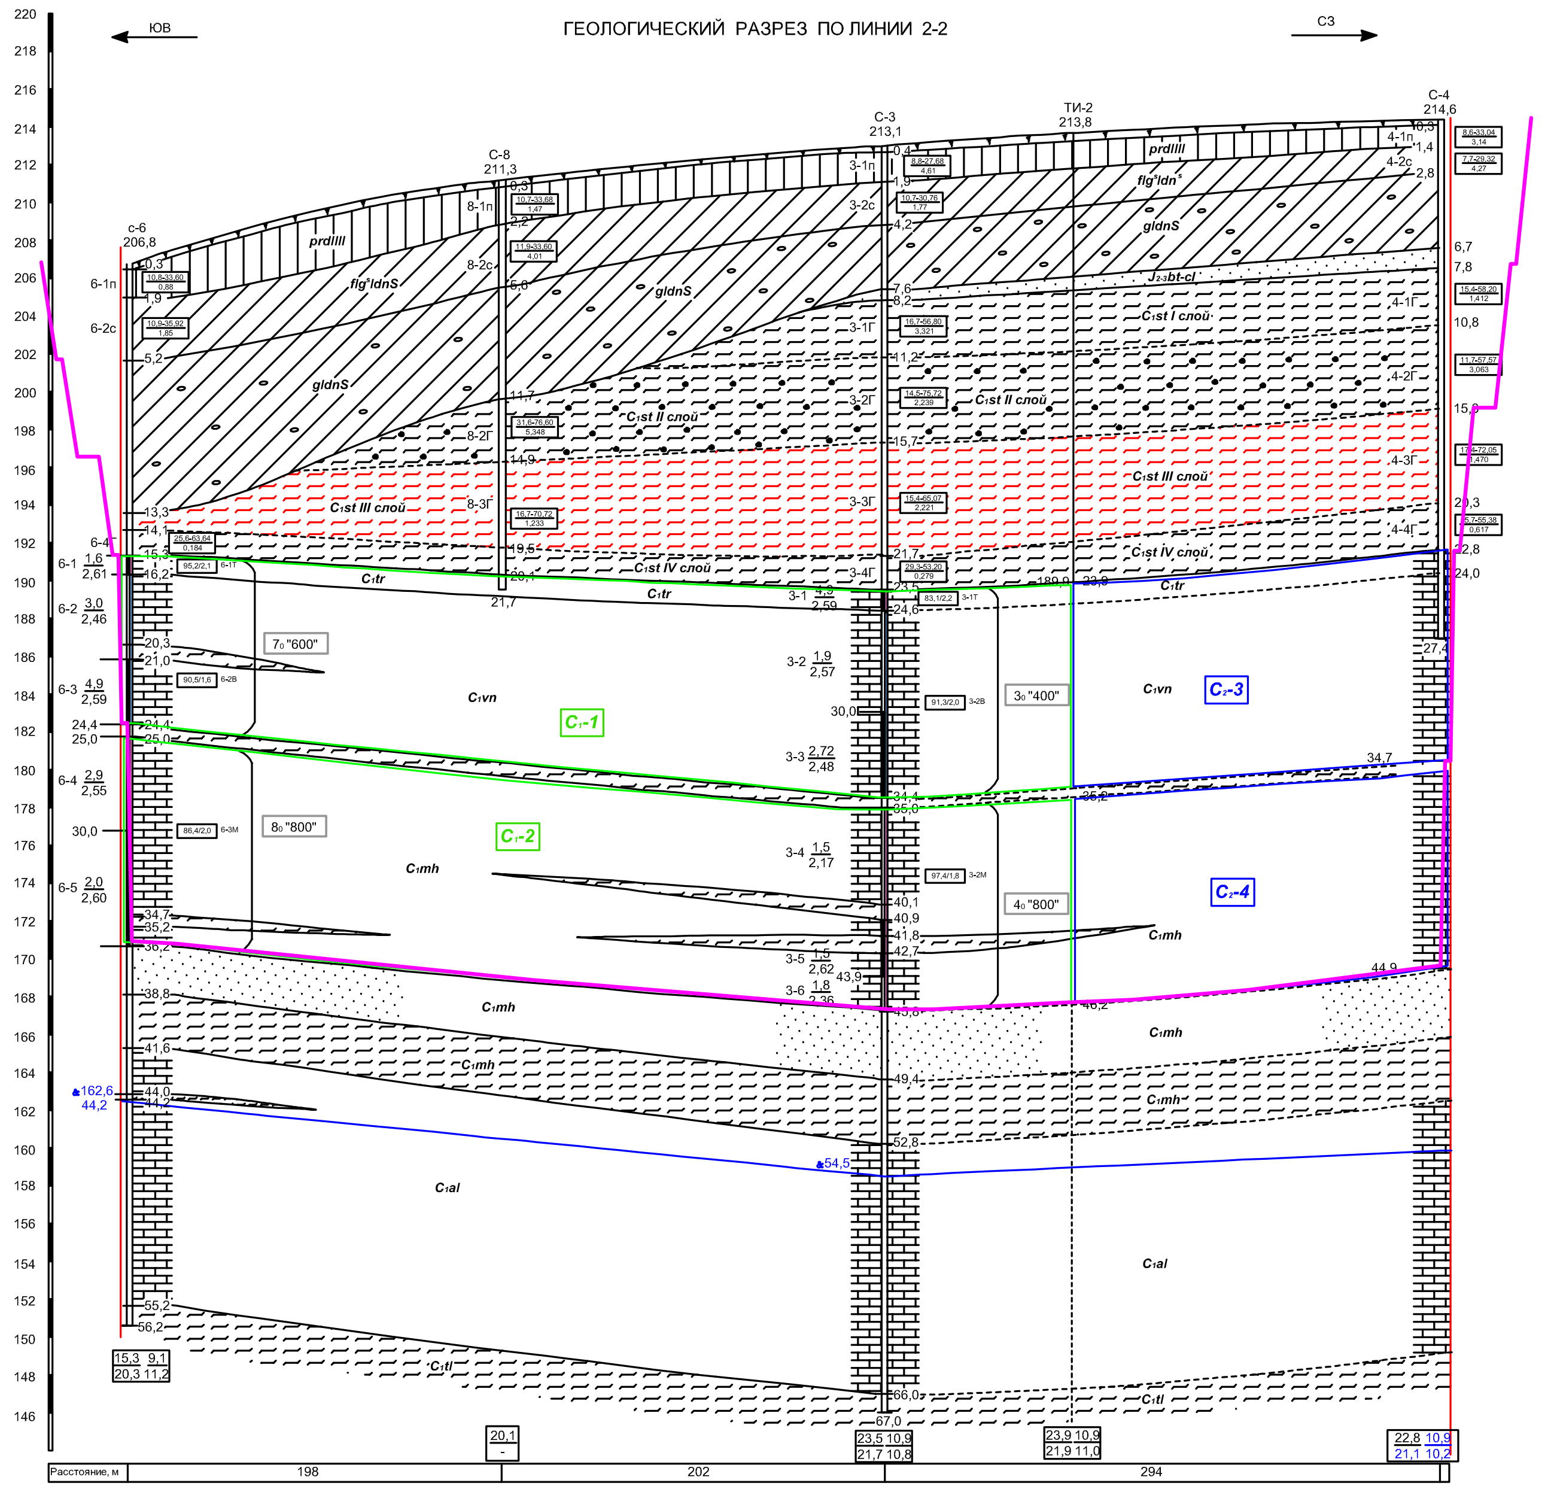

ГЕОЛОГИЧЕСКИЙ РАЗРЕЗ ПО ЛИНИИ III-III

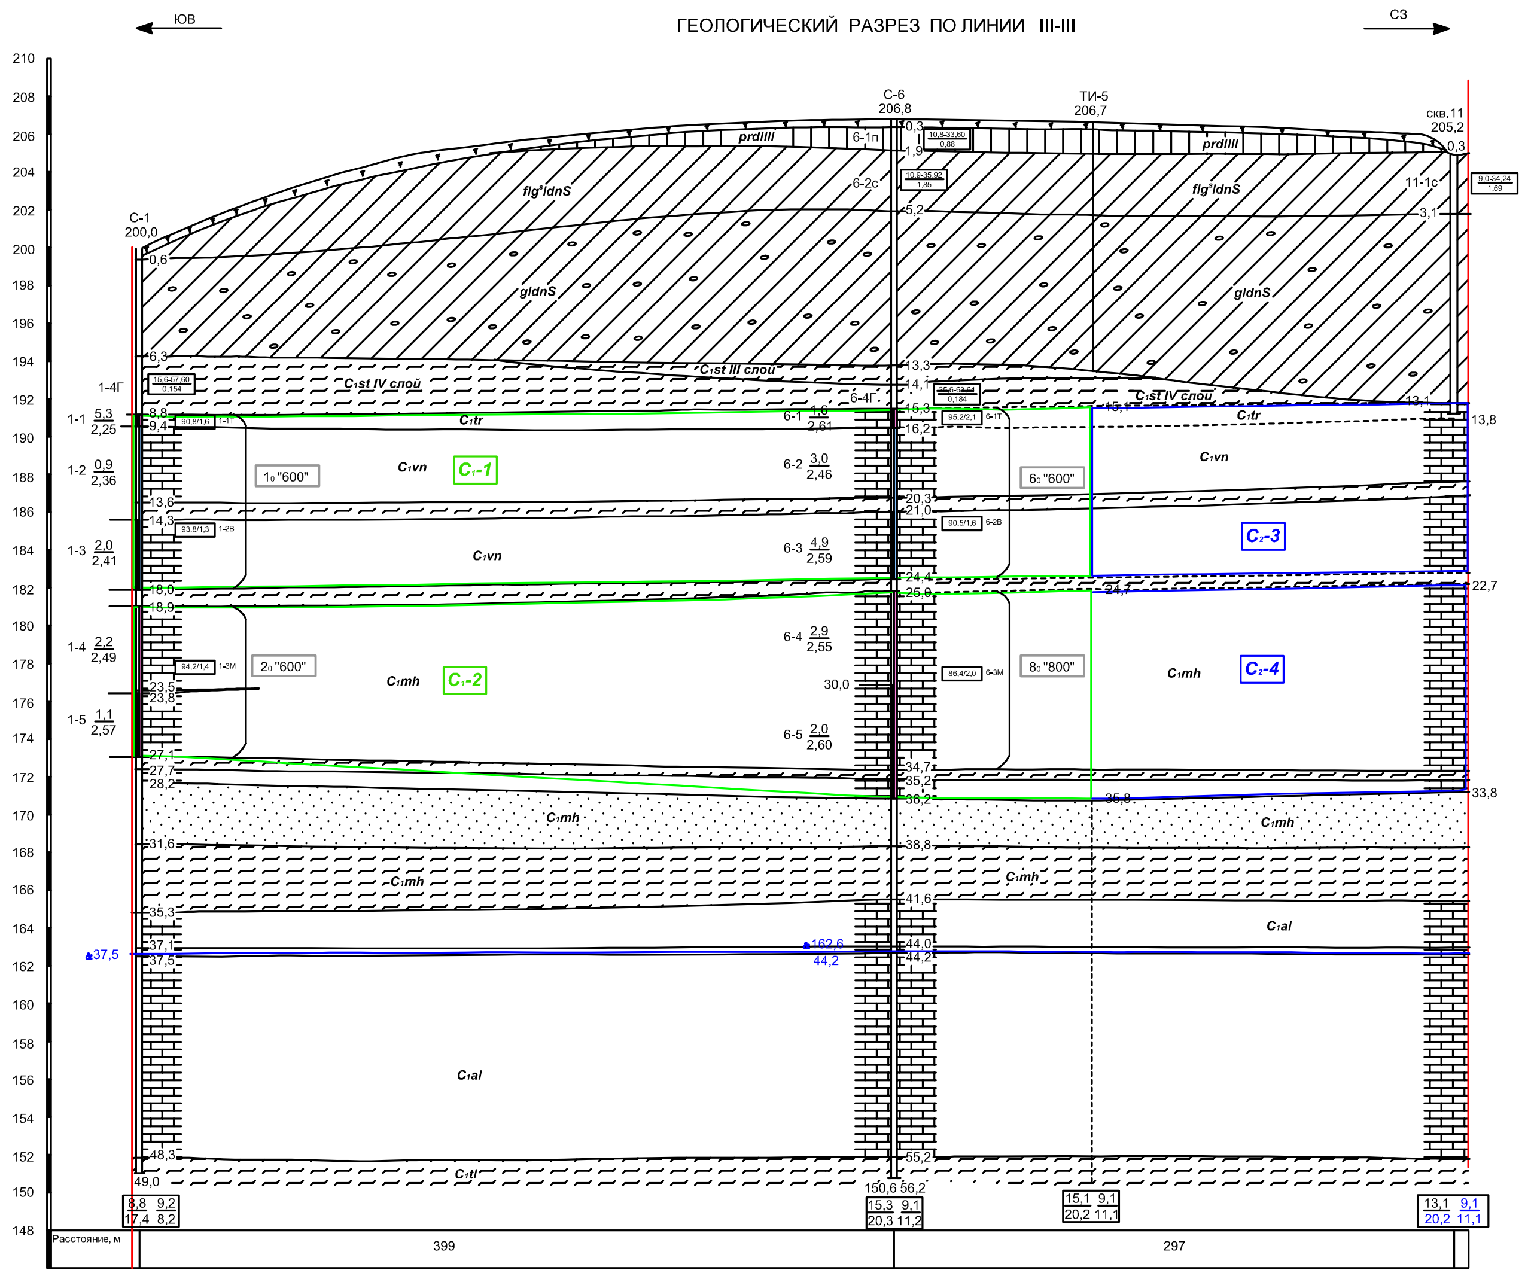

ГЕОЛОГИЧЕСКИЙ РАЗРЕЗ ПО ЛИНИИ IV-IV

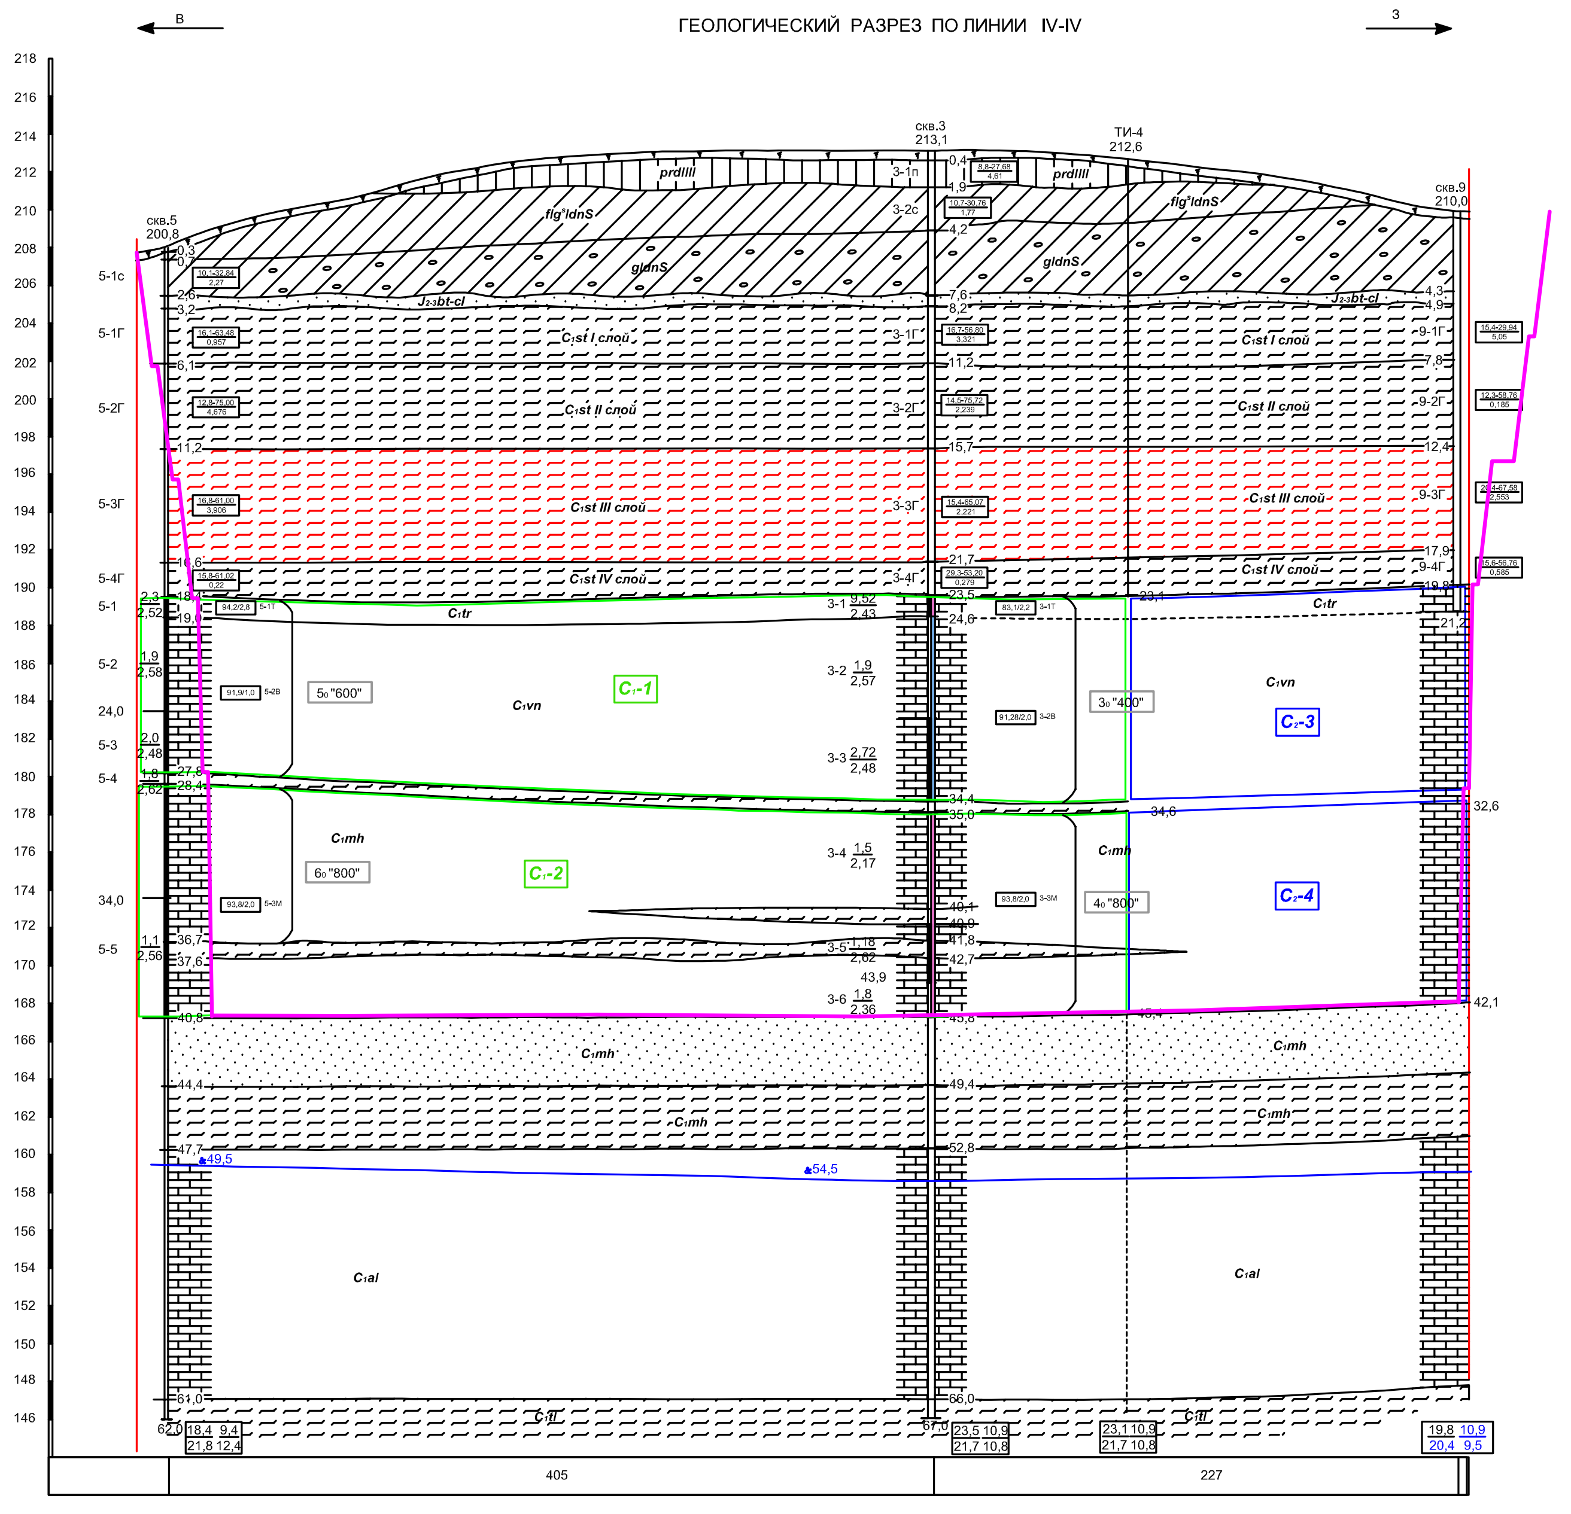

Условные обозначения

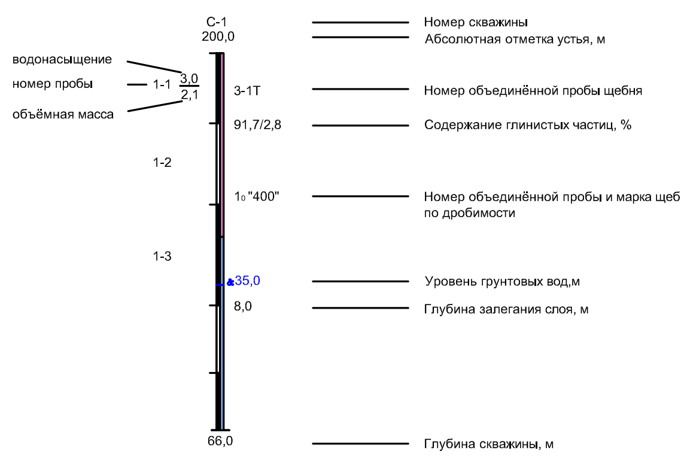
водонасыщение
номер пробы
объёмная масса
С-1
200,0
1-1
3,0
2,1
3-1Т
91,7/2,8
1-2
1₀"400"
1-3
35,0
8,0
66,0
Номер скважины
Абсолютная отметка устья, м
Номер объединённой пробы щебня
Содержание глинистых частиц, %
Номер объединённой пробы и марка щебня по дробимости
Уровень грунтовых вод,м
Глубина залегания слоя, м
Глубина скважины, м

Сечение, вошедшее в подсчёт запасов

Мощность вскрышных пород, м — 23,1 — Мощность известняков тарусско-венёвского горизонта, м

Общая мощность полезной толщи, м — 21,7 10,8 — Мощность известняков михайловского горизонта, м

ТИ-4 — Точка интерполяции и её номер

212,6 — Абсолютная отметка поверхности, м

Мощность вскрышных пород, м — 19,8 10,9 — Мощность известняков тарусско-венёвского горизонта, принятая к подсчету запасов категории C₂, м

Общая мощность полезной толщи, принятая к подсчету запасов категории C₂ — 20,4 9,5 — Мощность известняков михайловского горизонта, принятая к подсчету запасов категории C₂, м

Породы вскрыши

4-1п 1,2 2,4 — интервал опробования и номебра рядовых проб покровных суглинков

4-1с 3,4 — интервал опробования и номера рядовых проб моренных суглинков

4-1Г 6,6 — интервал опробования и номера рядовых проб стешевских глин

глины стешевского горизонта

15,7-55,38 / 0,617 — число пластичности; дисперсность; содержание CaCO₃ + MgCO₃, % к весу глины

суглинки покровные и надморенные

15,7-55,38 / 3,14 — число пластичности; дисперсность; содержание природных крупнозернистых включений в суглинках,%

🟥 Контур предварительного горного отвода

🟩 Контур подсчета запасов категории C₁

🟦 Контур подсчета запасов категории C₂

Контур конечного положения карьера

C₁-1 — Категория запасов и номер подсчетного блока

- ▨ Почвенно-растительный слой
- prdIII Суглинок покровный
- flgˢldnˢ Суглинок надморенный
- gldnS Суглинок моренный
- J₂₋₃bt-cl Пески (бат-келловейские отложения)
- C₁st Глины I слой
- C₁st Глины II слой
- C₁st Глины III слой
- C₁st Глины IV слой
- C₁tr Известняки тарусского горизонта
- C₁vn Известняки венёвского горизонта
- C₁mh Известняки михайловского горизонта
- C₁mh Пески (отложения михайловского горизонта)
- C₁mh Глины (отложения михайловского горизонта)
- C₁al Известняки алексинского горизонта
- C₁tl Глины отложения тульского горизонта

					ООО Сельскохозяйственное предприятие "Агротехпром"
Изм.	Лист	№ докум	Подпись	Дата	Разработка и рекультивация Марухтинского -2 месторождения строительных известняков
Маркшейдер		Телков Ю.В.			Геологические разрезы по линиям 1-1, 2-2, 3-3, 4-4.
					Стадия: ТП · Лист: 2 · Лислов: 1
					Масштабы: горизонтальный 1:2000 вертикальный 1:200
					ООО НПП "Центр-недра"