ГЕОЛОГИЧЕСКИЙ РАЗРЕЗ ПО ЛИНИИ V-V

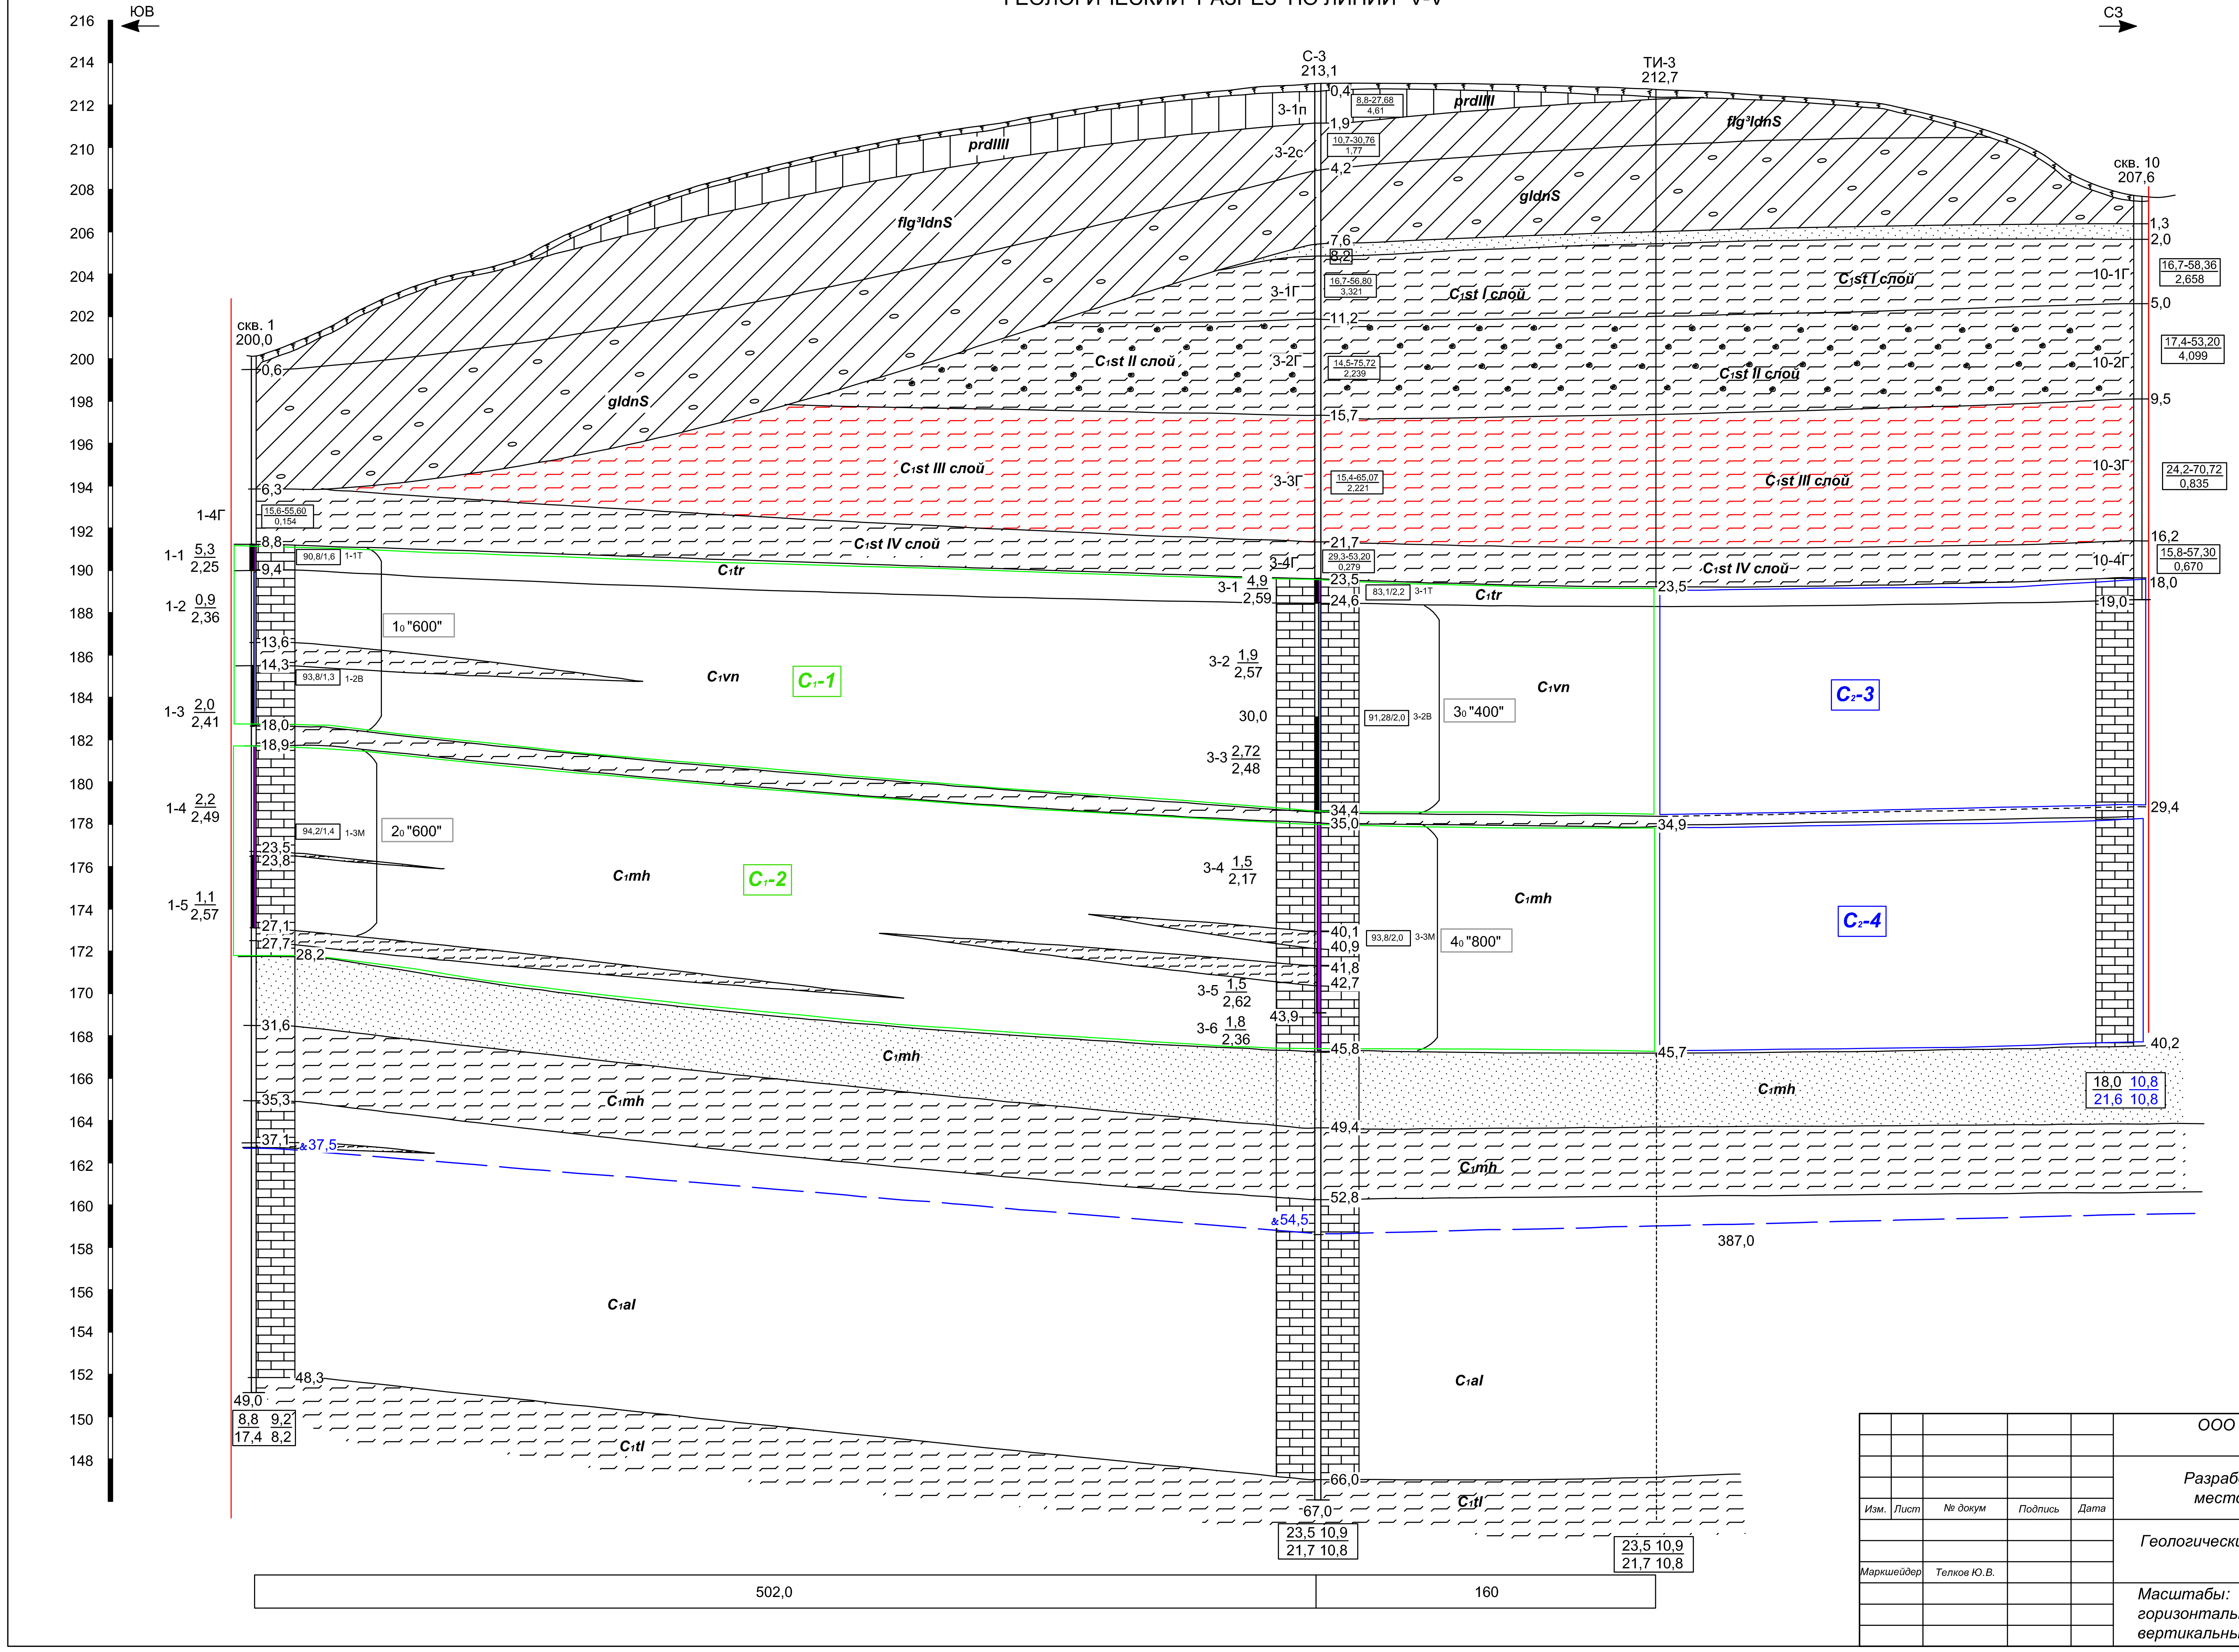

					ООО Сельскохозяйственное предприятие "Агротехпром"
					Разработка и рекультивация Марухтинского -2 месторождения строительных известняков
Изм.	Лист	№ докум	Подпись	Дата	

				Геологический разрез по линии 5-5.	Стадия	Лист	Лислов
Маркшейдер	Телков Ю.В.				ТП	3	1
				Масштабы: горизонтальный 1:2000 вертикальный 1:200	ООО НПП "Центр-недра"		